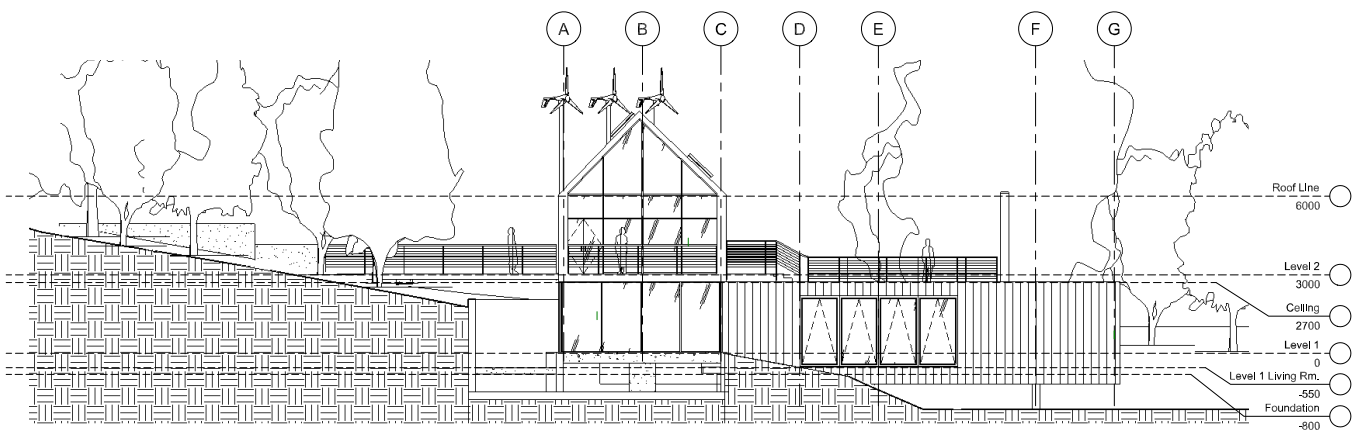

2 West
1 : 100

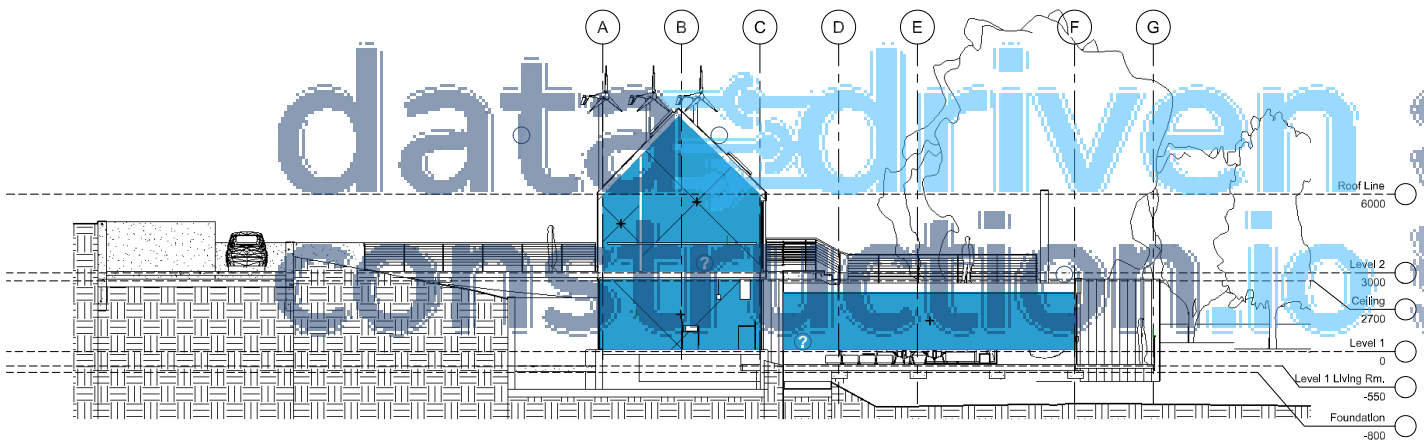

1 Building Section
1 : 100

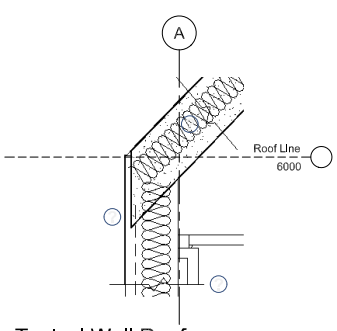

4 Typical Wall Roof Connection
1 : 10

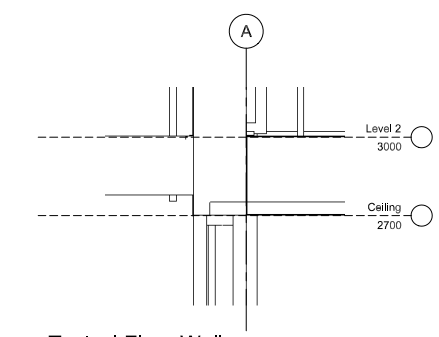

5 Typical Floor Wall Connection
1 : 10

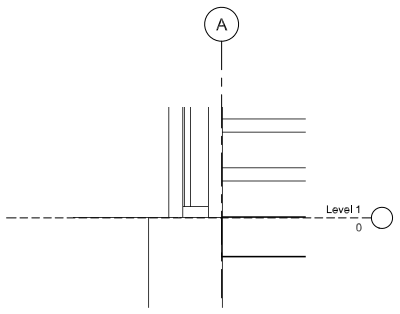

6 Typical Foundation Detail
1 : 10

3 Typ. Wall Section
1 : 20

data driven construction.io
community version
get the full version to remove this watermark

AUTODESK.

www.autodesk.com/revit

Consultant
Address
Address
Phone
Fax
e-mail

Consultant
Address
Address
Phone
Fax
e-mail

Consultant
Address
Address
Phone
Fax
e-mail

Consultant
Address
Address
Phone
Fax
e-mail

No.	Description	Date

Autodesk

Sample House

Elev./Sec./Det.

Project number	001-00
Date	Issue Date
Drawn by	SM
Checked by	JLH

A104

Scale As indicated

16.06.2025 00:10:59

DataDrivenConstruction.io - created in community version